

GENERAL NOTES

THE SCOPE AND LIMIT OF THIS SURVEY WAS DEFINED IN AUGUST, 2025 BY ANDREW & CAROL MCDONALD. USE OF THIS SURVEY IS LIMITED TO THE PROPERTY OWNER AS REFERENCED IN THE TITLE BLOCK AND CONSULTANTS FOR THE SPECIFIC PROJECT. OTHERS MAY NOT USE THIS MAP WITHOUT THE PERMISSION OF THE CLIENT AND HUMANN COMPANY. BOUNDARY AND BASIS OF BEARINGS ARE PER THE UNDERLYING RECORD MAP AS REFERENCED IN THE TITLE BLOCK HEREON.

TITLE REPORT FOR THIS SURVEY WAS PREPARED BY OLD REPUBLIC TITLE COMPANY, DATED APRIL 4, 2018, ORDER NO.0112015423-BJ. BOUNDARY AS SHOWN IS PER LOT LINE ADJUSTMENT LIA 2018-002 RECORDED NOVEMBER 15, 2016, DOCUMENT NO. 2016-246614, CONTRA COSTA COUNTY RECORDERS OFFICE.


THE ELECTRONIC FILE IF SUPPLIED, IS BEING DONE SO AS A COURTESY AND CONVENIENCE, AND IS SUBORDINATE TO THE PROVIDED SIGNED HARD COPY MAP WITH RESPECT TO CONTENT, ACCURACY AND QUALITY. HUMANN COMPANY MAKES NO WARRANTY OR GUARANTEE, EXPRESSED OR IMPLIED FOR ANY COPIES OF THE DRAWINGS OR WORK ASSOCIATED WITH THE ELECTRONIC FILE BY OTHERS.

BUILDING(S) SHOWN HEREON CONTAINS DECORATIVE ARCHITECTURAL ELEMENTS ALONG ITS WALLS AND CORNERS WHICH ARE NOT NECESSARILY ACCOUNTED FOR IN THE BUILDING FOOTPRINT AS SURVEYED AND MAPPED. PRIOR TO THE PREPARATION OF WORKING DRAWINGS, THE ARCHITECT/DESIGNER SHOULD FIELD INSPECT ANY AREAS ON THE BUILDING WHERE AN ADDITION OR OTHER IMPROVEMENT IS EXPECTED TO OCCUR (IF SETBACKS OR OTHER CONSTRAINTS ARE AN ISSUE), AND CONSULT WITH THE SURVEYOR OR ENGINEER AS NEEDED.

TREES AND DRIP LINES AS SHOWN ARE LOCATED SUFFICIENTLY FOR GENERAL ARCHITECTURAL SITE PLANNING. ANY CONSTRUCTION ACTIVITY PLANNED IMMEDIATELY ADJACENT TO THE TREES OR DRIP LINES SHOULD BE REVIEWED WITH THE APPROPRIATE CONSULTANT. IF IT IS DETERMINED THAT DETAILED TREE AND/OR BRANCH MEASUREMENTS ARE NEEDED, FURTHER SURVEYING MAY BE NECESSARY AND SHOULD BE ARRANGED BY THE OWNER AND/OR CONSULTANT. SPECIES AS REFERENCED ON THE SURVEY SHOULD BE CONFIRMED BY A LICENSED ARBORIST OR LANDSCAPE ARCHITECT IF THE SPECIFIC TREE(S) IS SUSPECTED OF BEING A PROTECTED OR CRITICAL ONE(S).


DATUM: ELEVATIONS SHOWN HEREON ARE BASED UPON CENTRAL CONTRA COSTA SANITARY MANHOLE INVERT, AS SAID MANHOLE INVERT ELEVATION TAKEN AS 573.00 FEET.

CONTOUR INTERVAL: 2 FEET

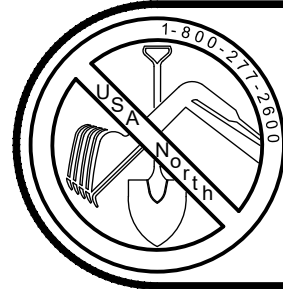



BEFORE EXCAVATING CALL U.S.A.

OWNER AND/OR CONTRACTOR ARE RESPONSIBLE FOR LOCATION AND VERIFICATION OF ALL EXISTING UNDERGROUND UTILITIES. UNDERGROUND SERVICE ALERT (USA) SHOULD BE NOTIFIED FOR ASSISTANCE IN THIS MATTER AT (800) 227-2600, 48 HOURS PRIOR TO ANY CONSTRUCTION. THE (USA) AUTHORIZATION NUMBER SHALL BE KEPT AT THE JOB SITE. LOCATION AND CHARACTER OF ANY UTILITIES IF SHOWN HEREON ARE APPROXIMATE AND TAKEN FROM A COMBINATION OF SURFACE STRUCTURE OBSERVATION AND/OR THE RECORDS OF THE CONTROLLING AGENCY. HUMANN COMPANY DOES NOT ASSUME RESPONSIBILITY FOR THE LOCATION OF ANY EXISTING UTILITIES OR OTHER UNDERGROUND FEATURES SUCH AS WALLS, TANKS, BASEMENTS, BURIED OBJECTS, ETC.

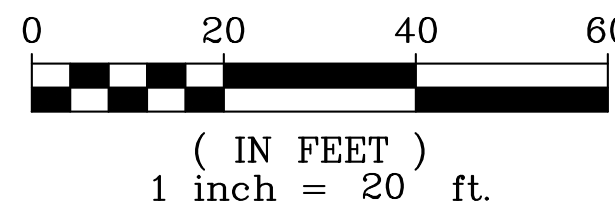

LEGEND

- MB MAIL BOX
- GUY WIRE
- JOINT POLE
- AREA DRAIN
- CATCH BASIN
- WATER VALVE
- FIRE HYDRANT
- WATER METER
- SEWER CLEAN OUT
- CATCH BASIN IN CURB
- SURVEY CONTROL POINT
- SANITARY SEWER LINE AND MAINHOLE
- EXISTING GRADE

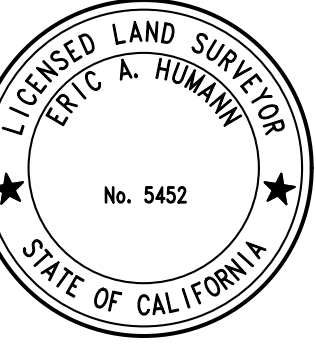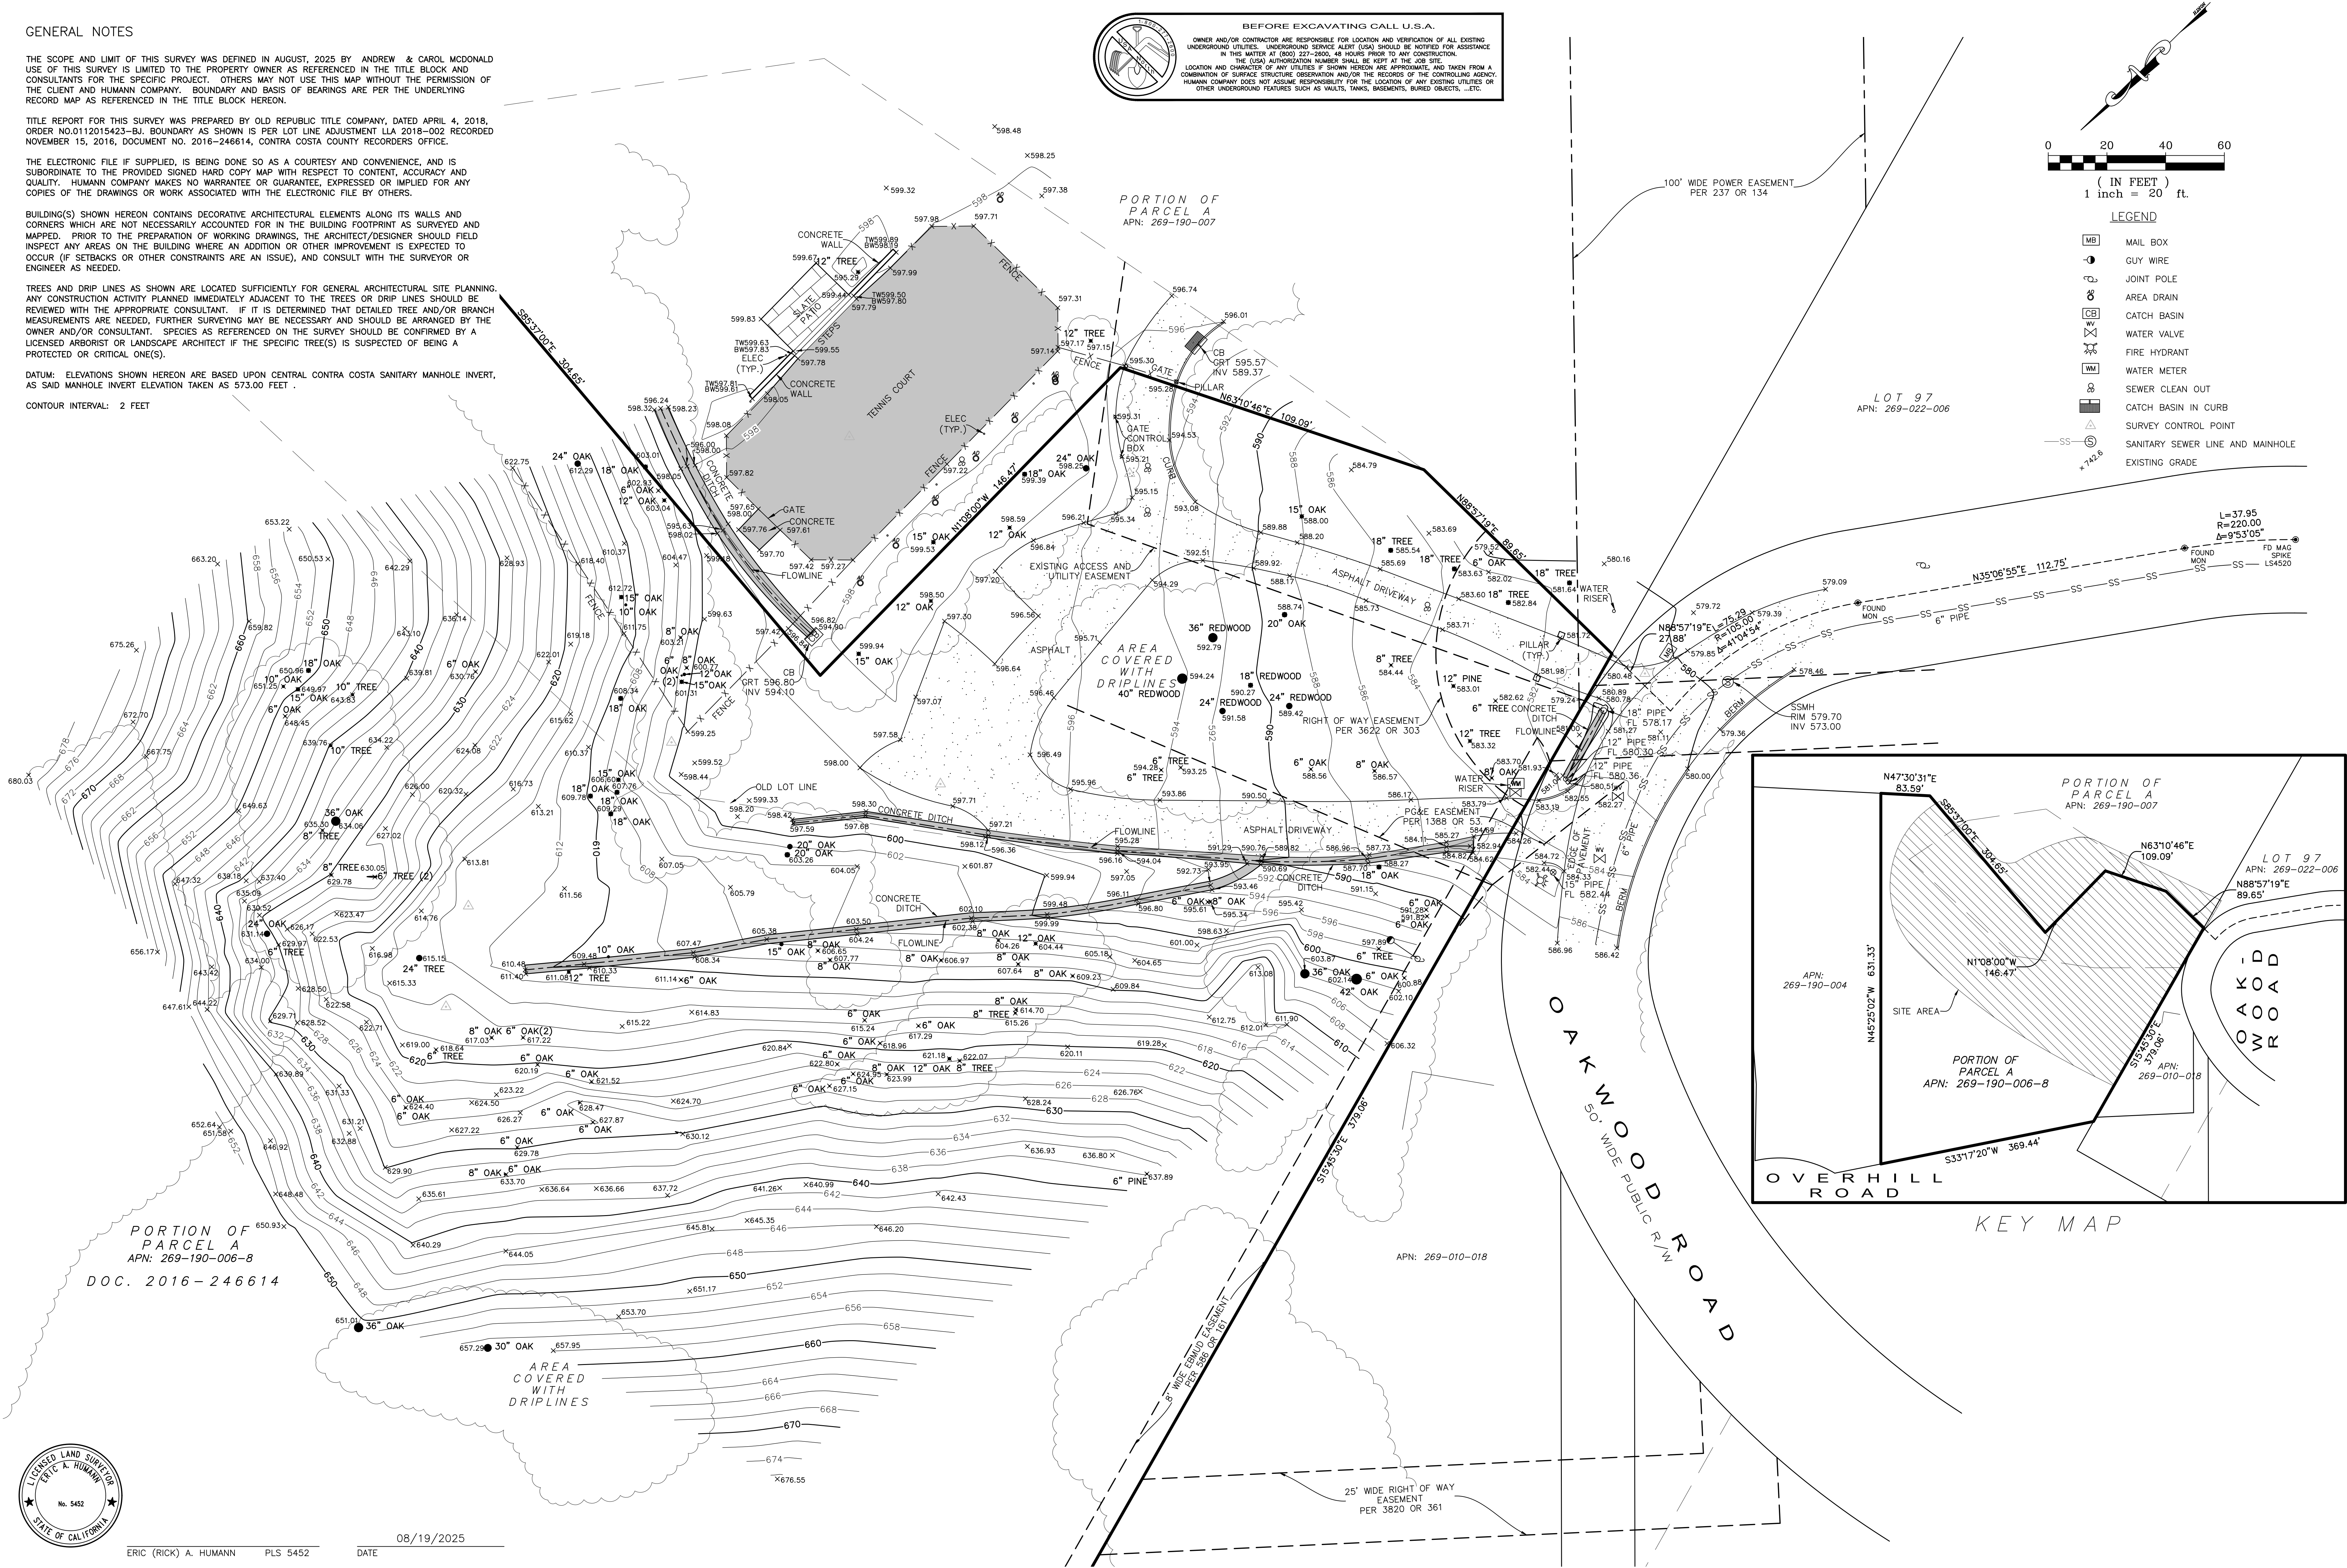

ERIC (RICK) A. HUMANN PLS 5452 DATE 08/19/2025

NO.	DATE	BY	REVISIONS

SCALE	1" = 20'
DATE	08/19/2025
DRAWN	ALDA/DS
CHECKED	RH
JOB NO.	18048



ERIC (RICK) A. HUMANN PLS 5452

PARTIAL TOPOGRAPHIC SURVEY
PORTION OF PARCEL A, MAP OF SUBDIVISION MSO 3-87, BOOK 130 & PAGE 4, CONTRA COSTA COUNTY
ANDREW & CAROL MCDONALD - - 38 OAKWOOD ROAD


ORINDA

CALIFORNIA



SHEET 1
OF 1 SHEETS

JOB NO. 18048

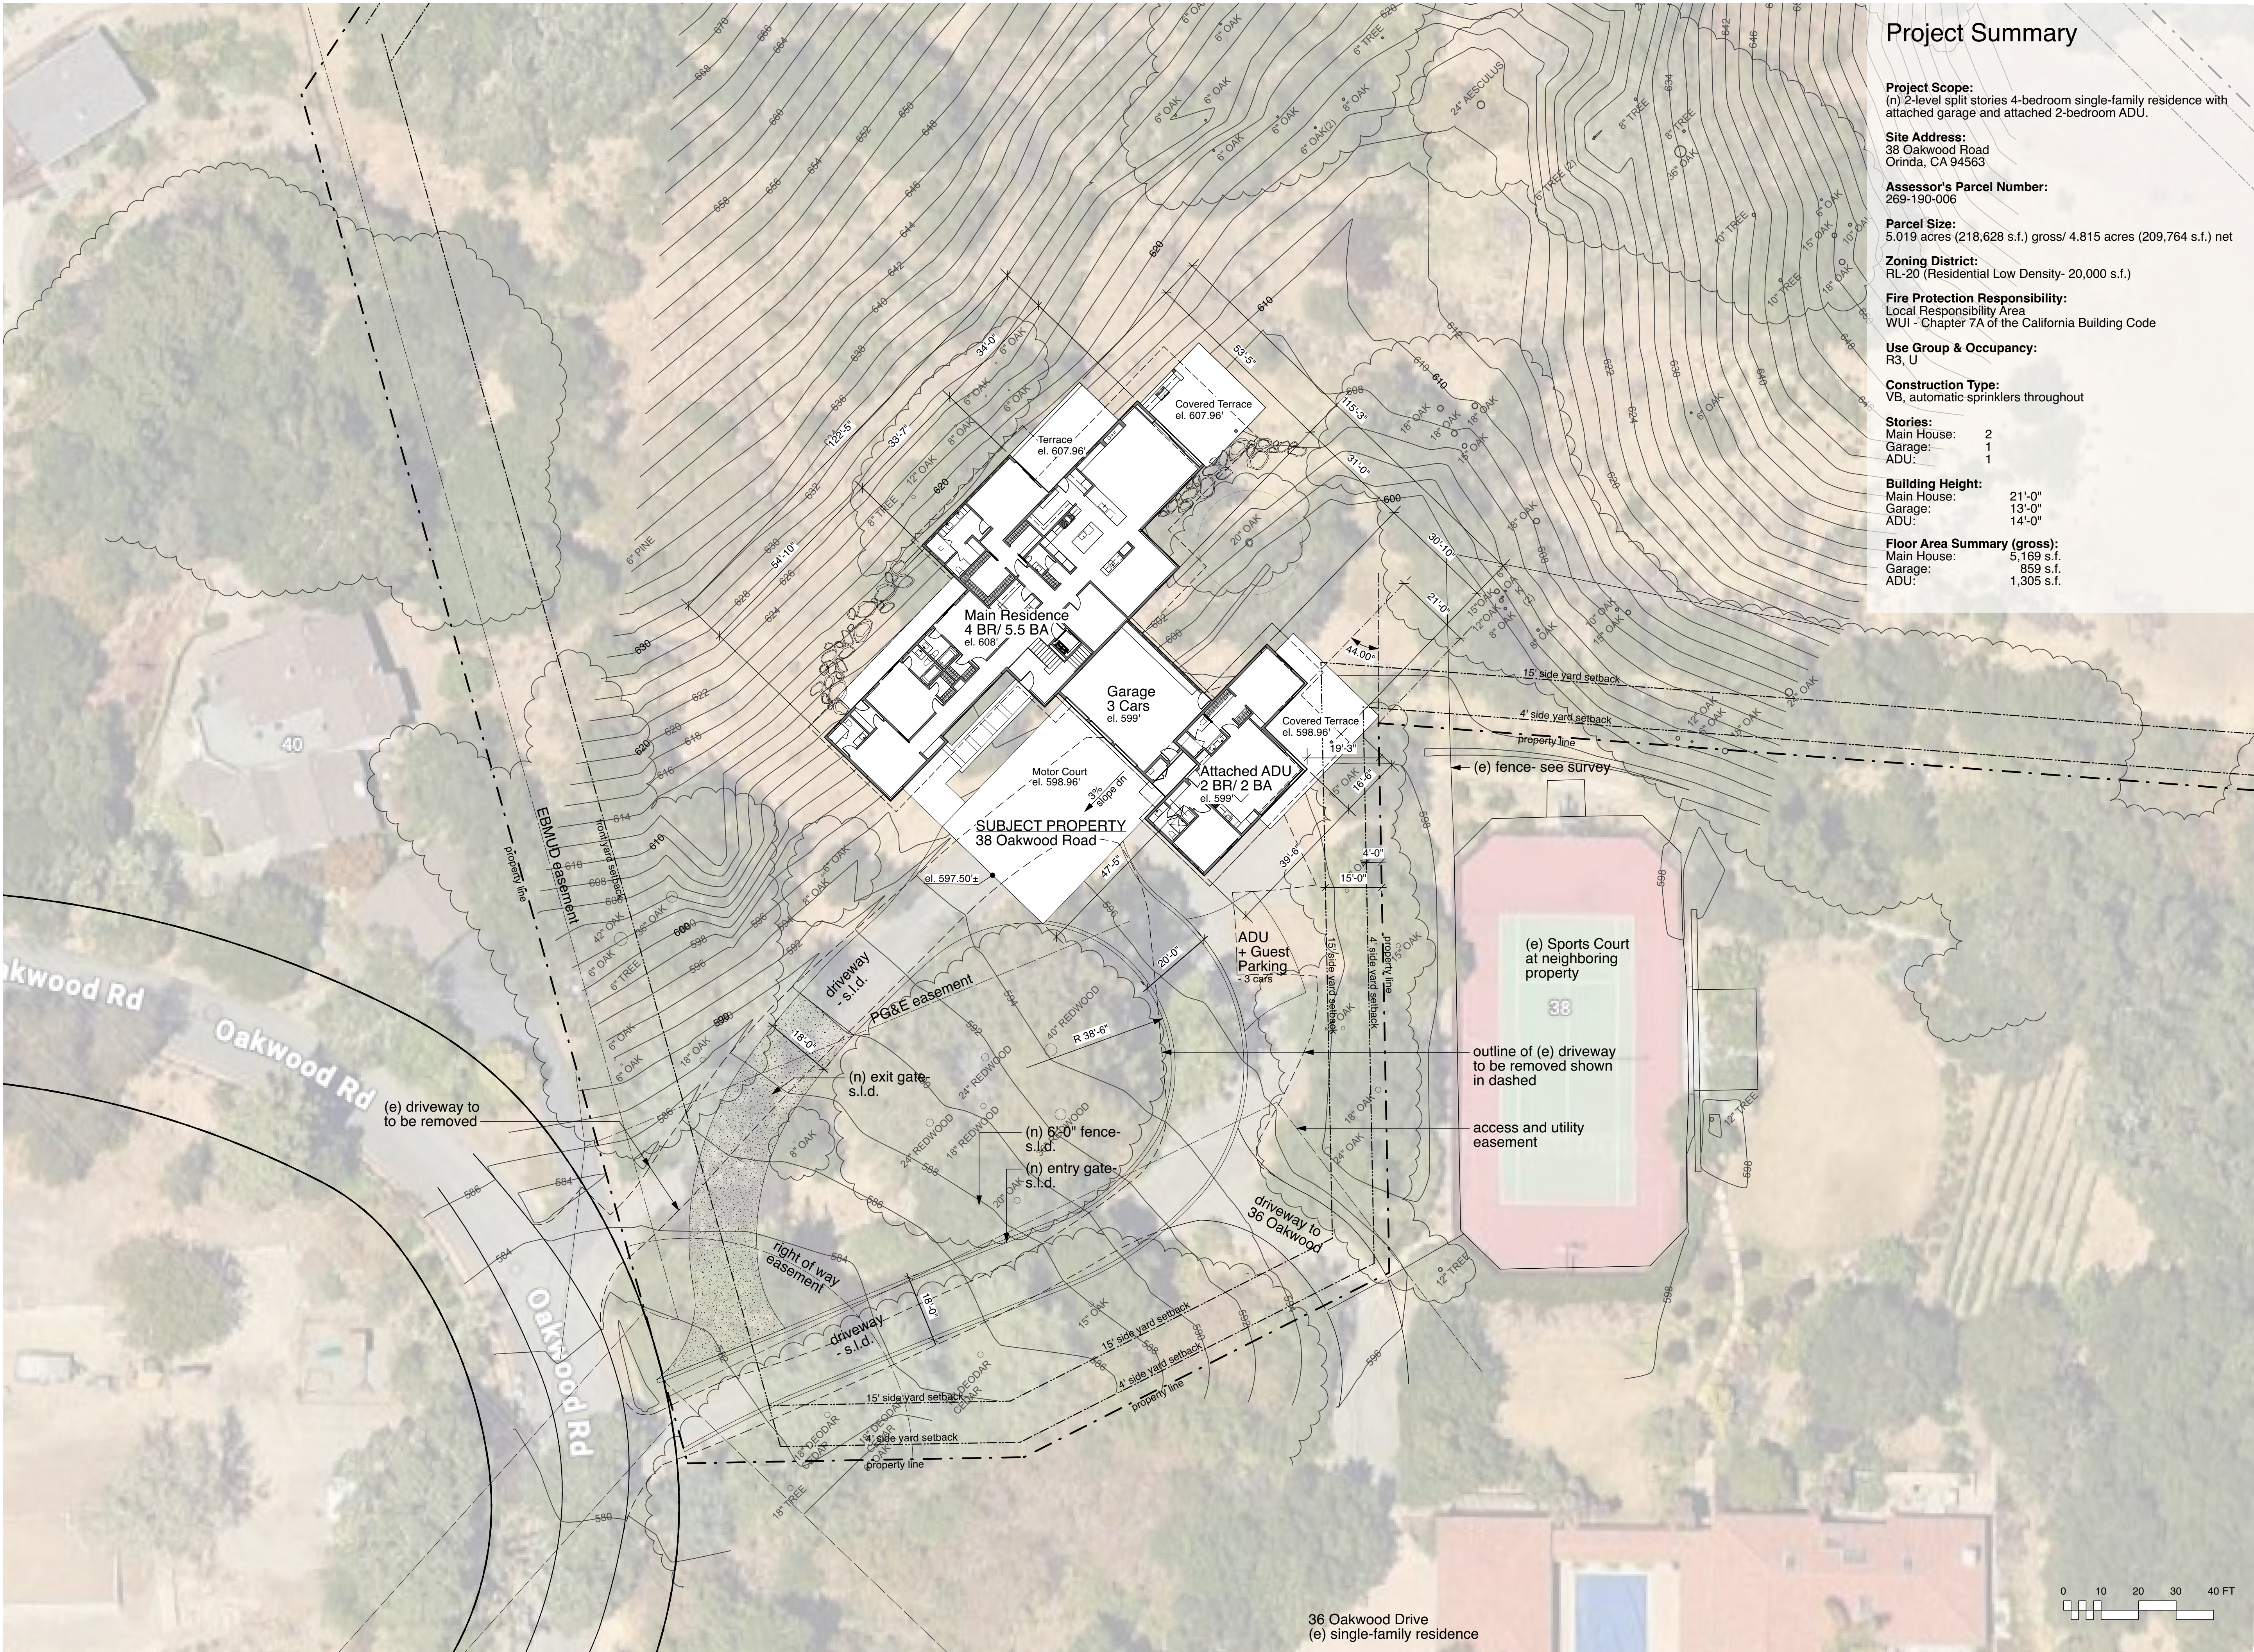

Project Summary

Project Scope:
(n) 2-level split stories 4-bedroom single-family residence with attached garage and attached 2-bedroom ADU.

Site Address:
38 Oakwood Road
Orinda, CA 94563

Assessor's Parcel Number:
269-190-006

Parcel Size:
5.019 acres (218,628 s.f.) gross/ 4.815 acres (209,764 s.f.) net

Zoning District:
RL-20 (Residential Low Density- 20,000 s.f.)

Fire Protection Responsibility:
Local Responsibility Area
WUI - Chapter 7A of the California Building Code

Use Group & Occupancy:
R3, U

Construction Type:
VB, automatic sprinklers throughout

Stories:
Main House: 2
Garage: 1
ADU: 1

Building Height:
Main House: 21'-0"
Garage: 13'-0"
ADU: 14'-0"

Floor Area Summary (gross):
Main House: 5,169 s.f.
Garage: 859 s.f.
ADU: 1,305 s.f.


Taylor
Lombardo
Architects

LLP


40 Hotaling Place
San Francisco
California 94111

(415) 433-7777 tel
(415) 433-7717 fax

taylorlombardo.com

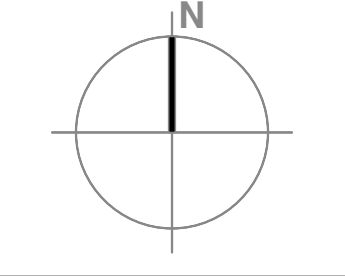

McDonald Residence
38 Oakwood Road
Orinda, CA 94563
APN 269-190-006

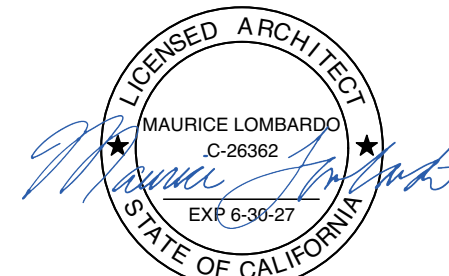

This drawing is the property of Taylor Lombardo Architects LLP. Any unauthorized use in part or in whole without written permission is prohibited.

Site Plan

scale: 1" = 20'-0"

revision: date:

Pre-Project Review 01.28.26

job no: 2512

drawn: FL

checked: TT

date: 01.28.26

sheet no:

A1.01